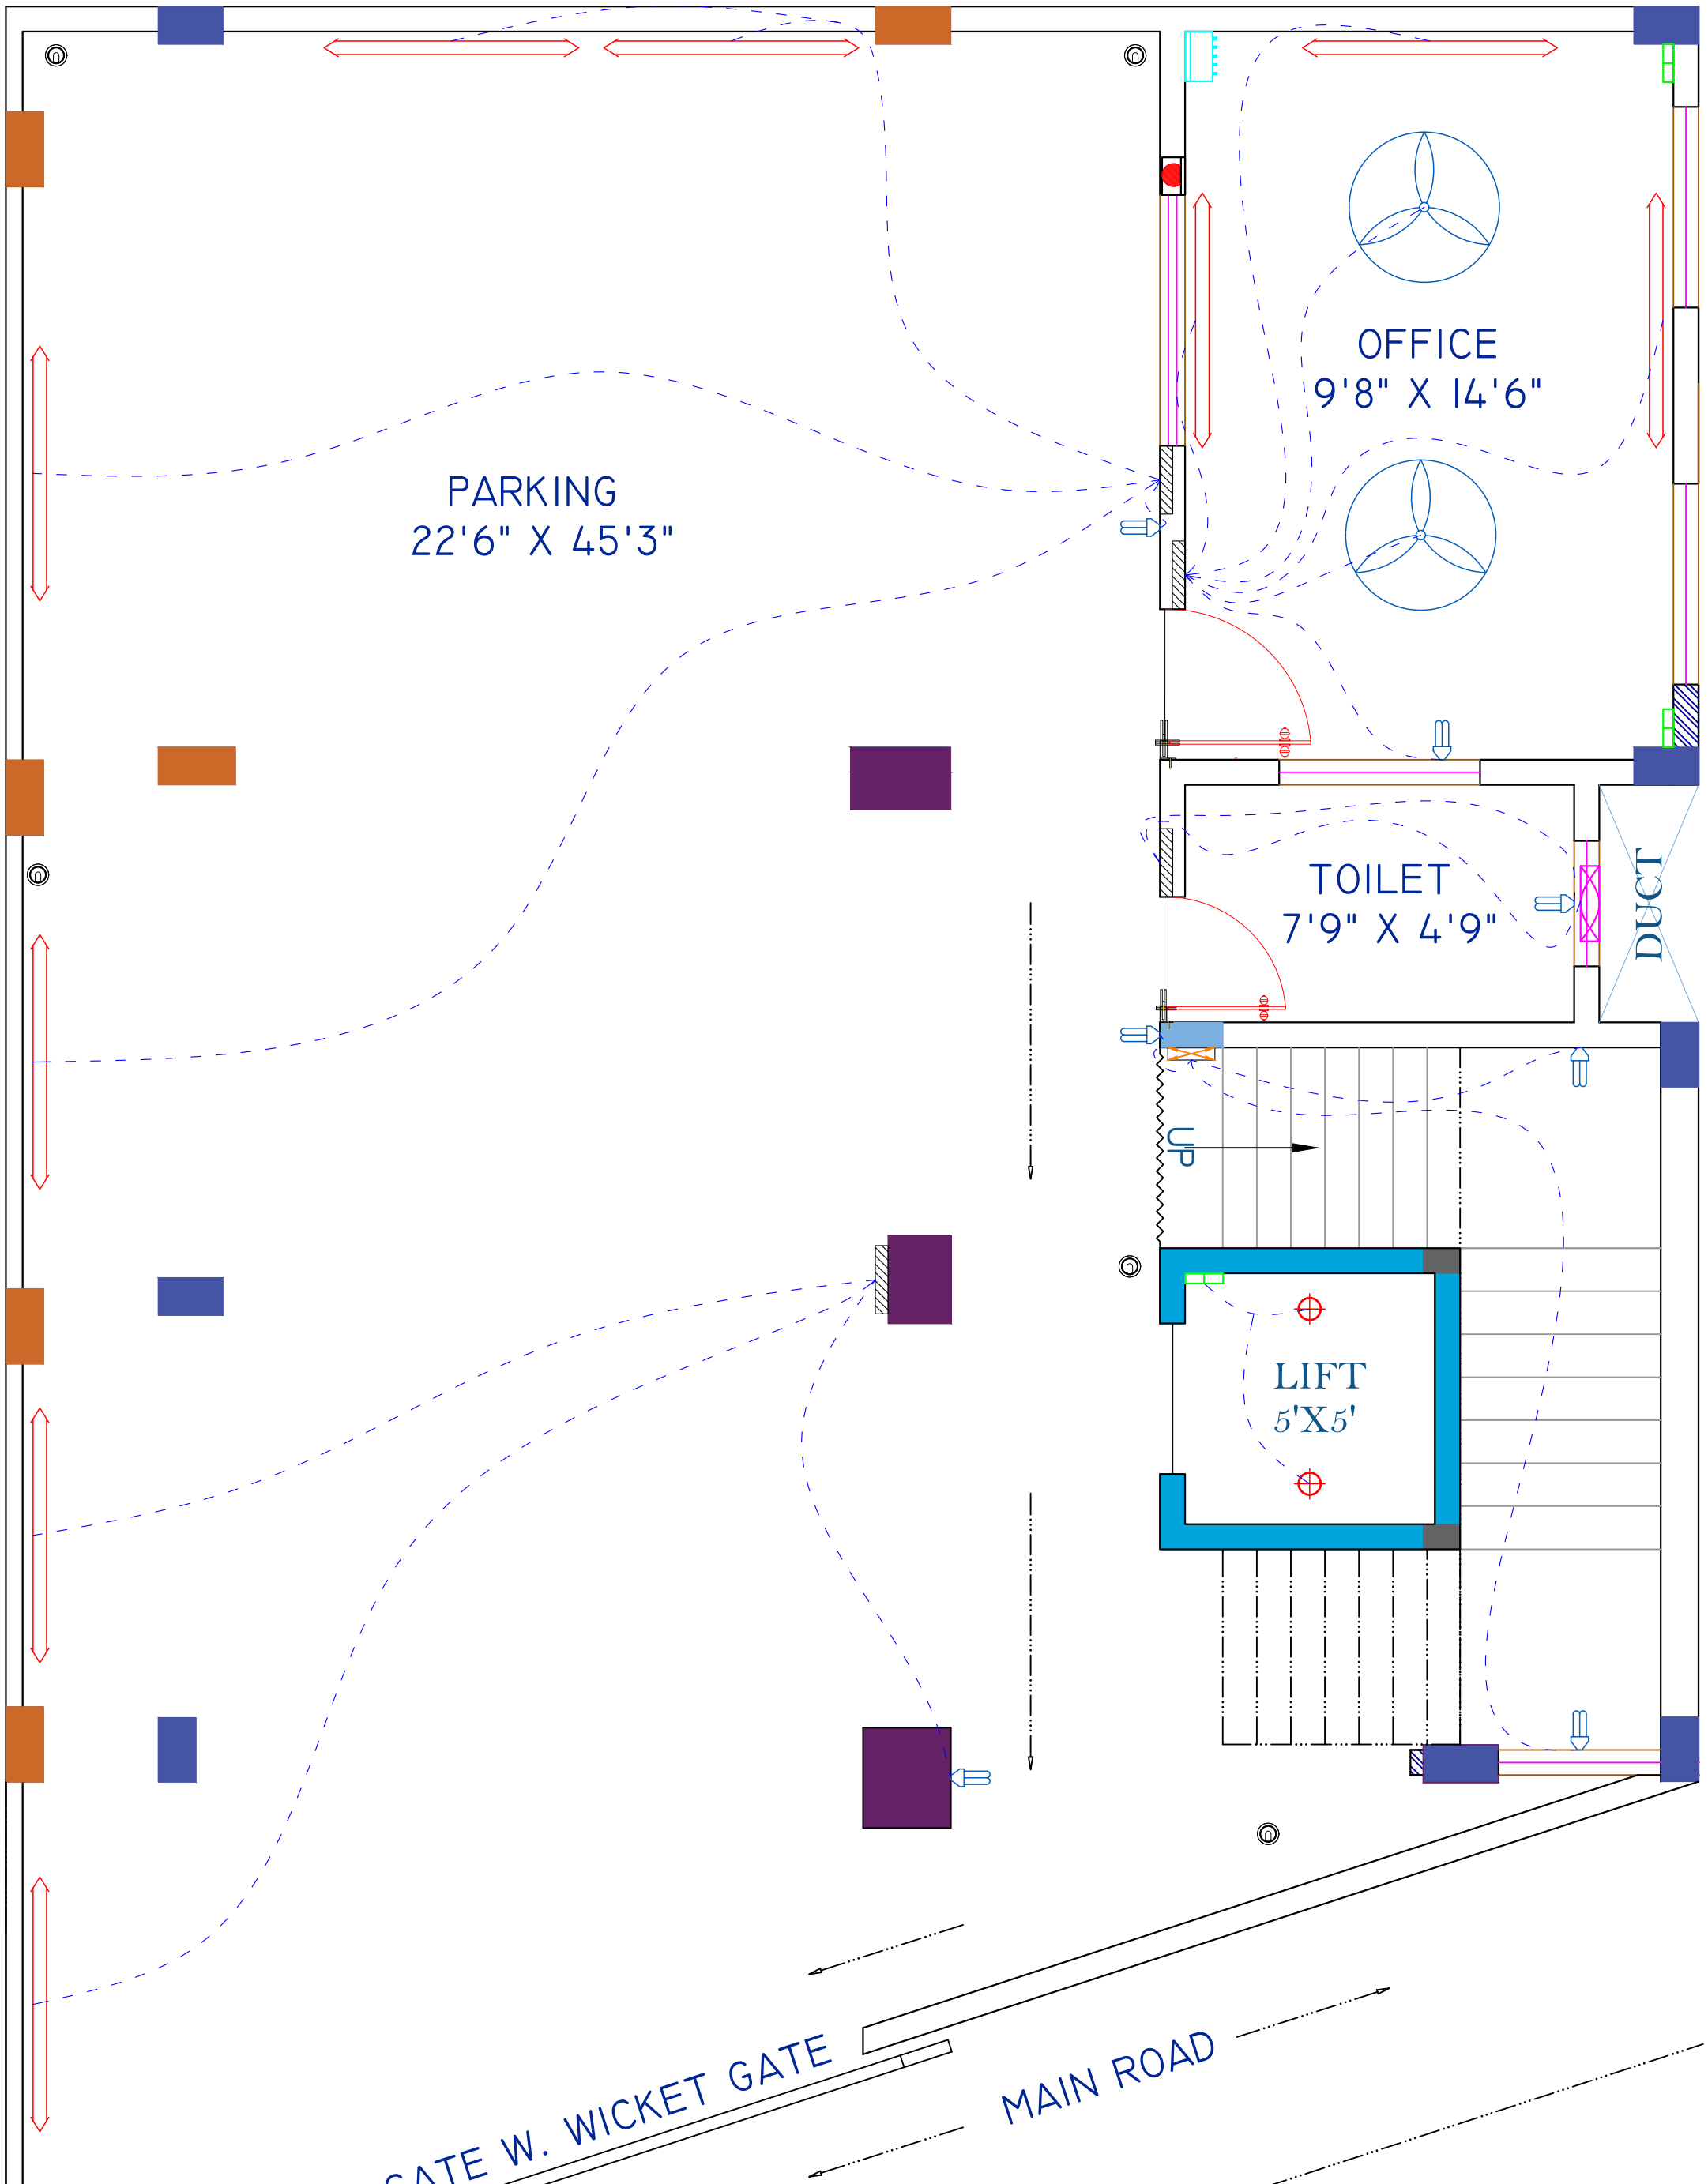

GROUND FLOOR PLAN

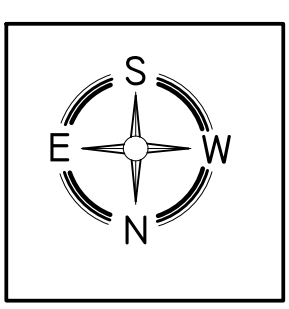

PROJECT DETAILS:-

PROPOSED GROUND FLOOR ARCHITECTURAL PLAN
FOR PROPOSED LIBRARY /
MAULANA MAUDUDI MEMORIAL FOUNDATION BUILDING
CTS NO.:-
SITUATED AT SARAFA BAZAR, SHAHGUNJ
TQ. & DIST. AURANGABAD, MAHARASHTRA.

FOR:-JAMAAT-E-ISLAMI HIND, AURANGABAD.

CONSULTANT

INFINITY & ASSOCIATES
ATTRIBUTES OF AUTHENTICITY
•PLANNER •RCC DESIGNER •VALUER
1st Floor, Opp. Tirupati Enclave, Silk Mills Colony, Aurangabad - 431001.
Email: inscribeinfinity@gmail.com
Web: www.infinityally.com
M : +91 9225 796 225 | +91 9422972767

SHEET NO:- 01/05

DATE:- 09 JULY 2024 | REV. : 00

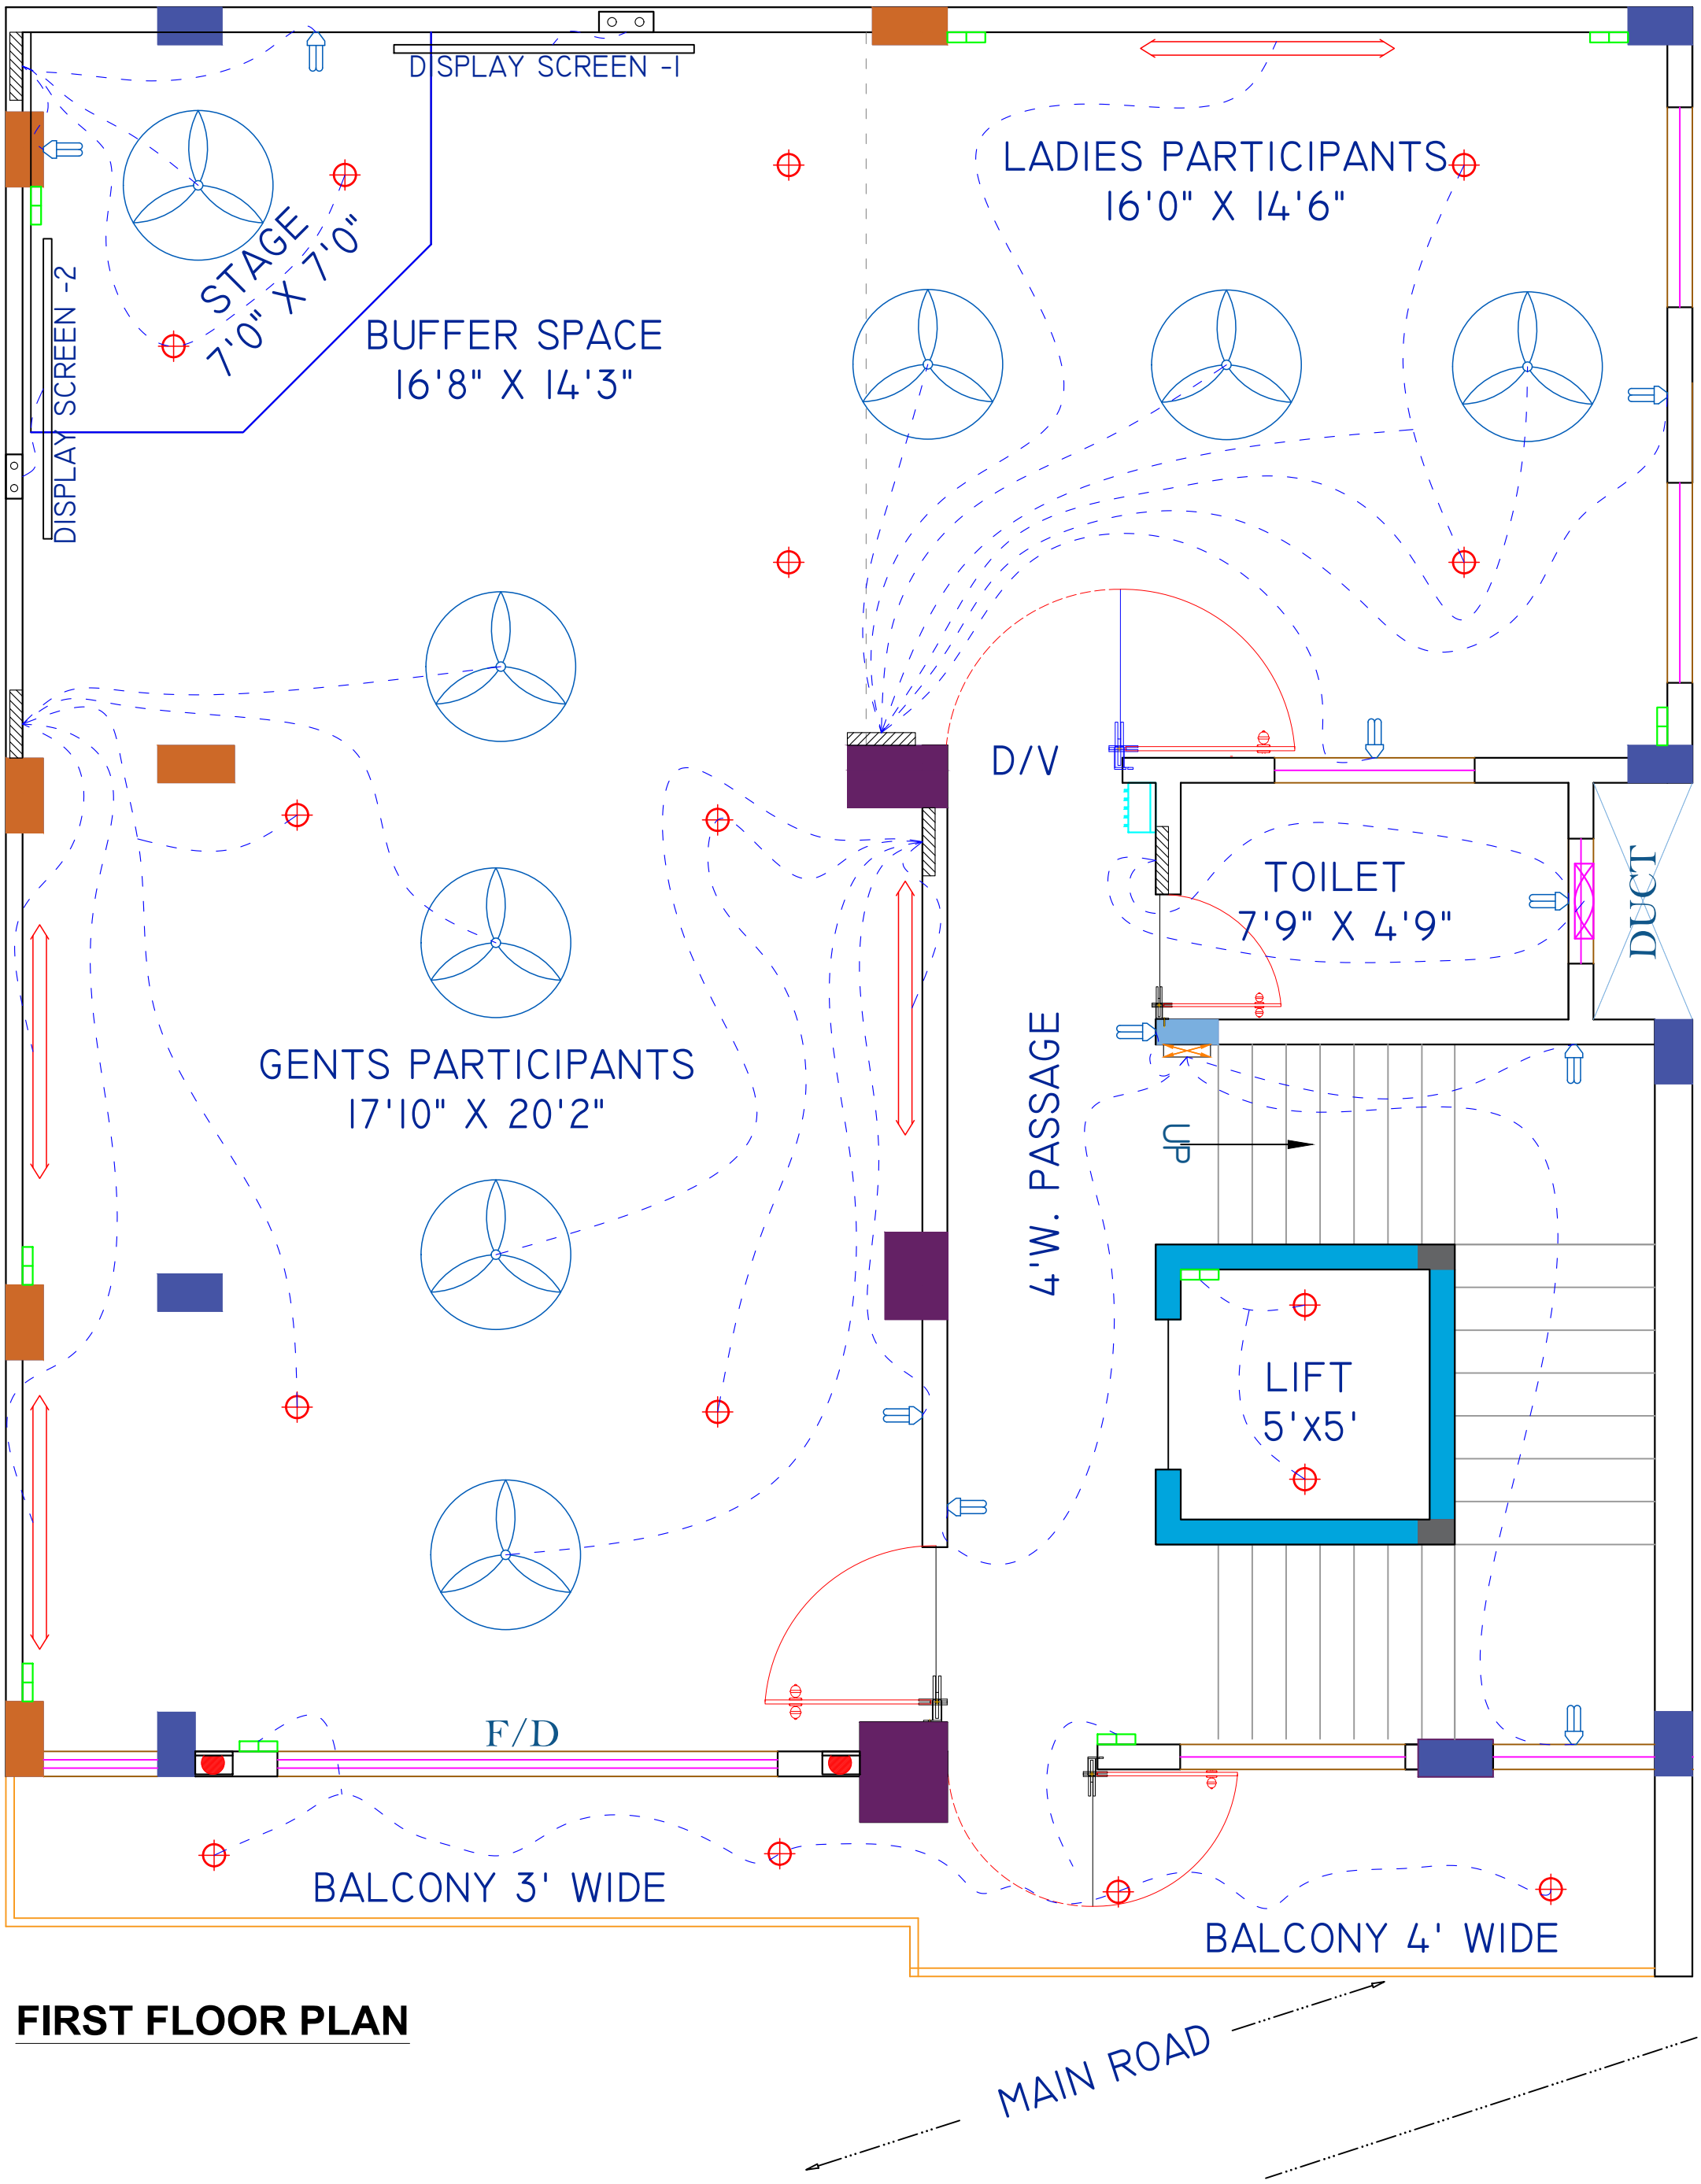

FIRST FLOOR PLAN

S
E W
N

GENERAL NOTE'S:-

PROJECT DETAILS:-

PROPOSED FIRST FLOOR ARCHITECTURAL PLAN
FOR PROPOSED LIBRARY /
MAULANA MAUDUDI MEMORIAL FOUNDATION BUILDING
CTS NO.:-
SITUATED AT SARAFA BAZAR, SHAHGUNJ
TQ. & DIST. AURANGABAD, MAHARASHTRA.

FOR:-JAMAAT-E-ISLAMI HIND, AURANGABAD.

SHEET NO:- 02/05

CONSULTANT

INFINITY & ASSOCIATES
ATTRIBUTES OF AUTHENTICITY
•PLANNER •RCC DESIGNER •VALUER
1st Floor, Opp. Tirupati Enclave, Silk Mills Colony, Aurangabad - 431001.
Email: inscribeinfinity@gmail.com
Web: www.infinityally.com
M : +91 9225 796 225 | +91 9422972767

DATE:- 09 JULY 2024 | REV. : 00

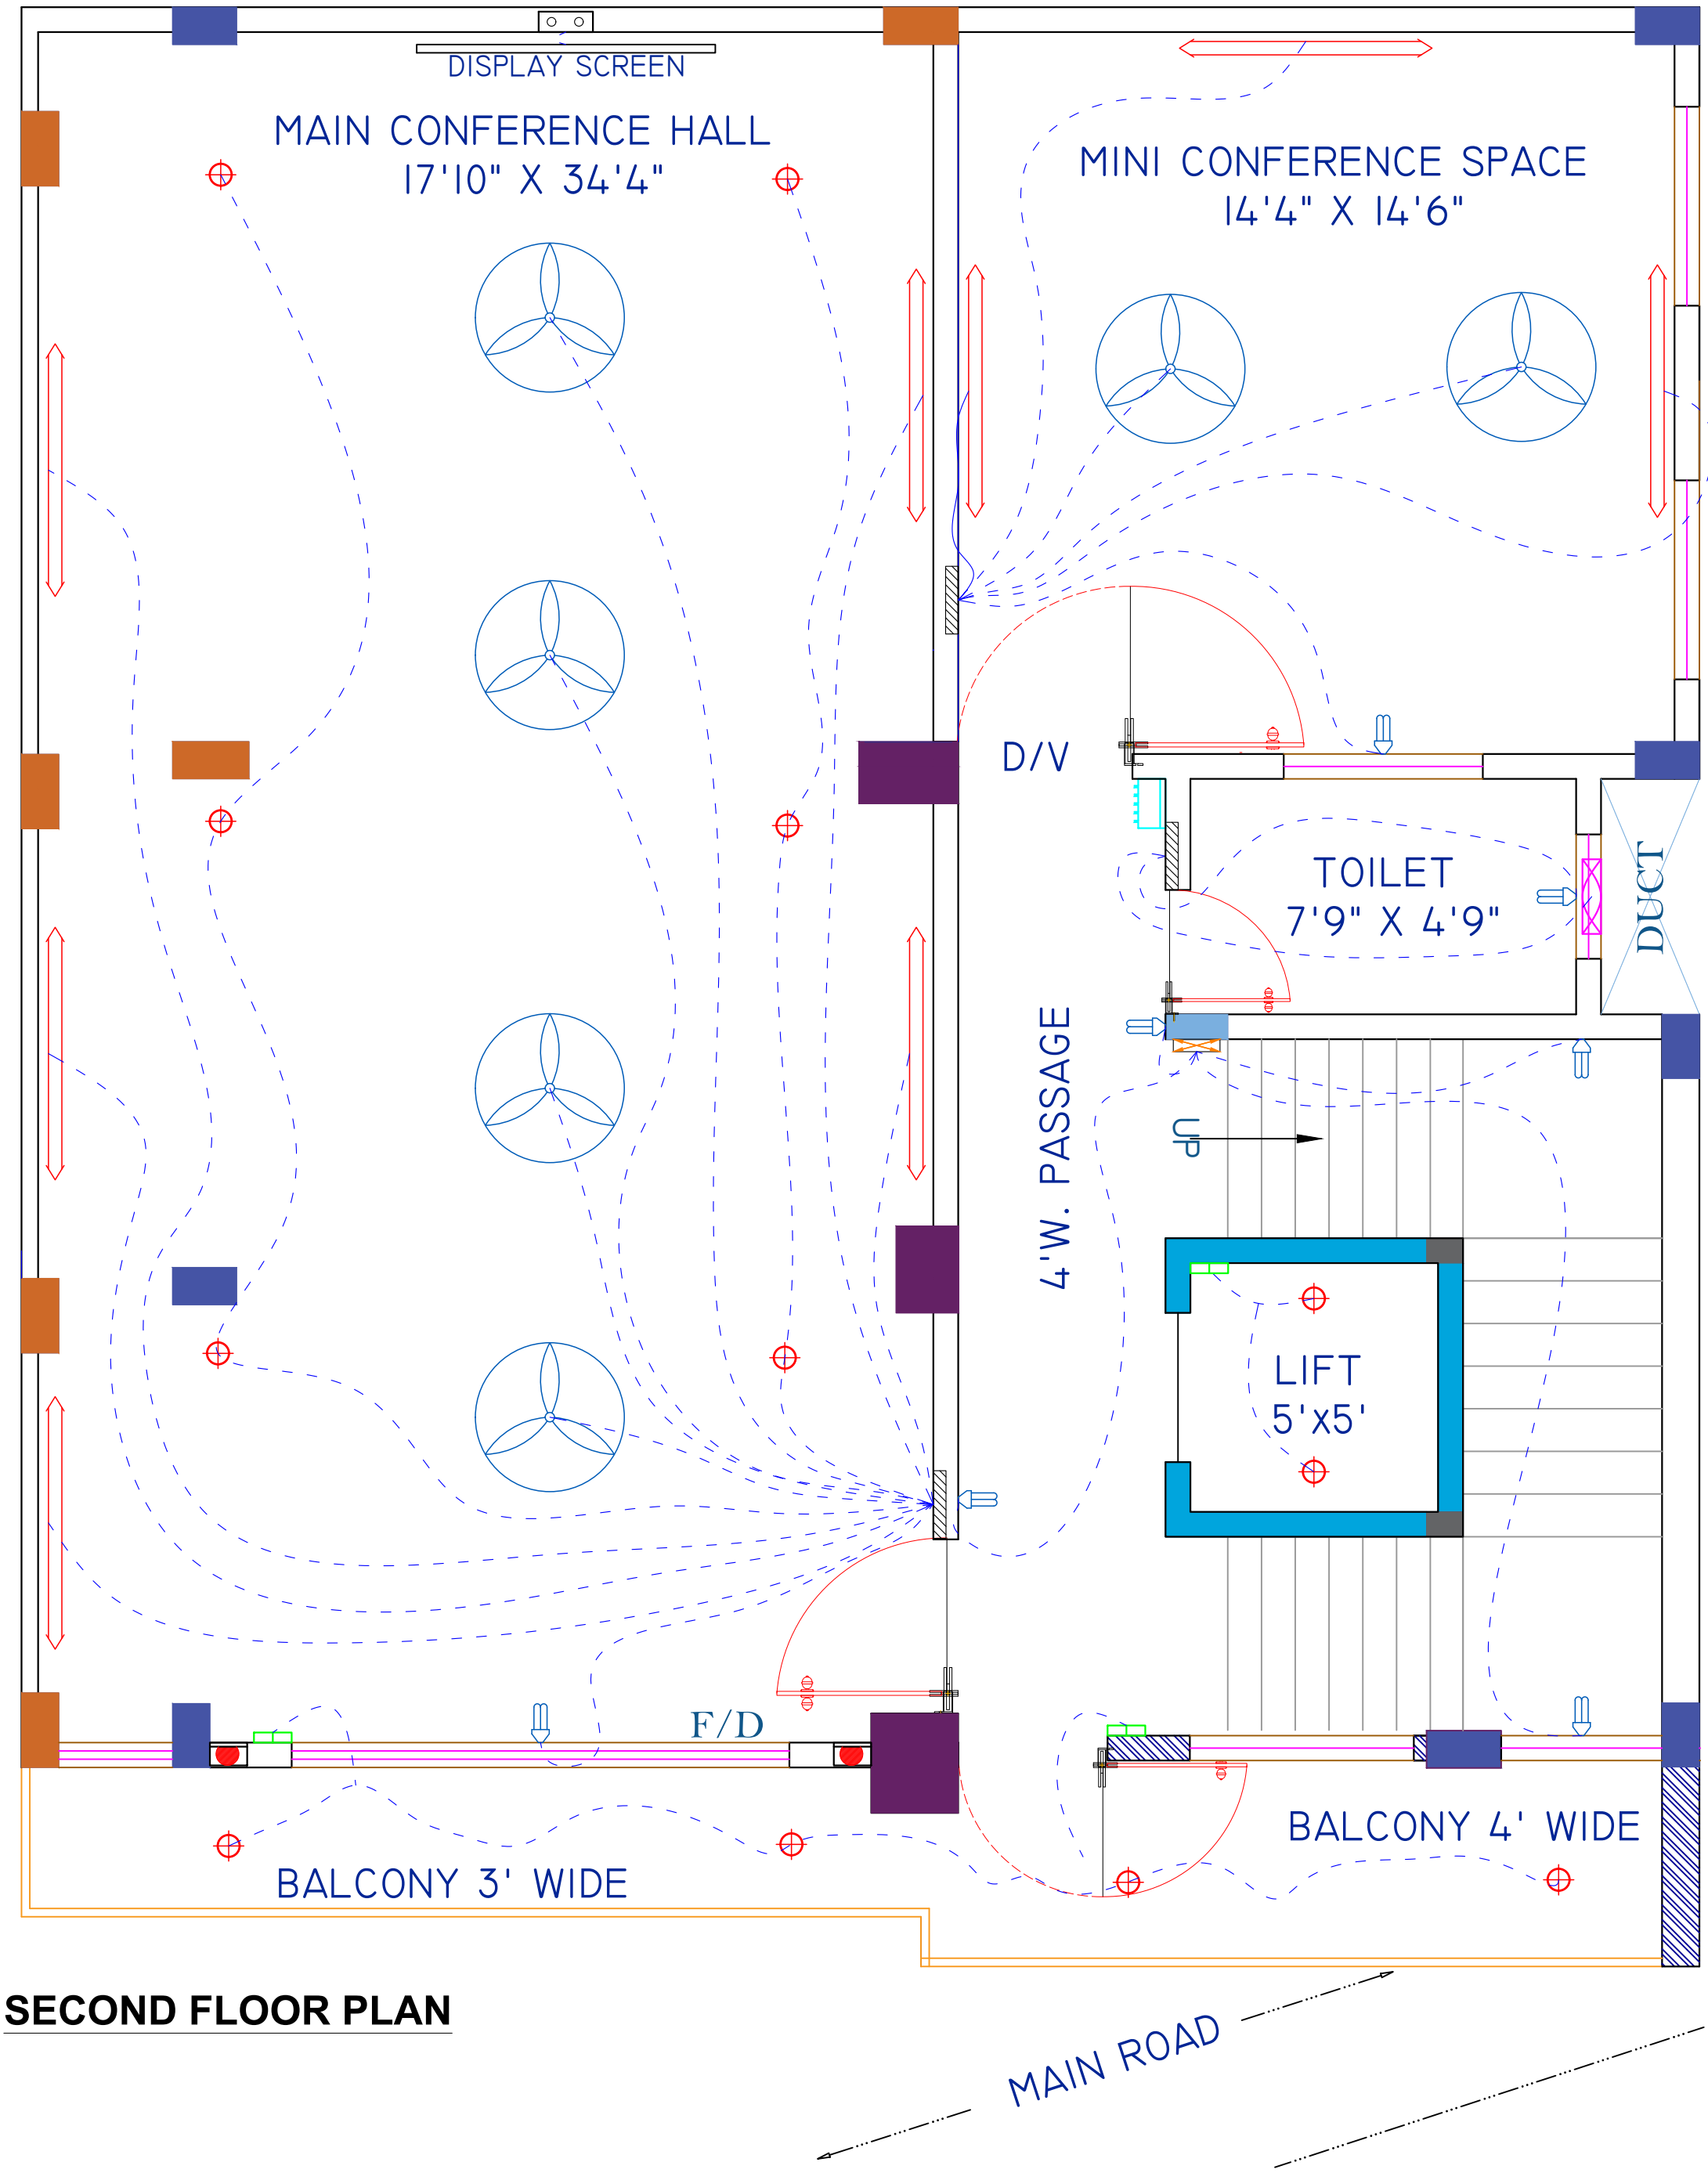

SECOND FLOOR PLAN

S
E W
N

GENERAL NOTE'S:-

PROJECT DETAILS:-

PROPOSED SECOND FLOOR ARCHITECTURAL PLAN
FOR PROPOSED LIBRARY /
MAULANA MAUDUDI MEMORIAL FOUNDATION BUILDING
CTS NO.:-
SITUATED AT SARAFA BAZAR, SHAHGUNJ
TQ. & DIST. AURANGABAD, MAHARASHTRA.

FOR:-JAMAAT-E-ISLAMI HIND, AURANGABAD.

CONSULTANT

INFINITY & ASSOCIATES
ATTRIBUTES OF AUTHENTICITY
•PLANNER •RCC DESIGNER •VALUER
1st Floor, Opp. Tirupati Enclave, Silk Mills Colony, Aurangabad - 431001.
Email: inscribeinfinity@gmail.com
Web: www.infinityally.com
M : +91 9225 796 225 | +91 9422972767

SHEET NO:- 03/05

DATE:- 09 JULY 2024 | **REV. :** 00

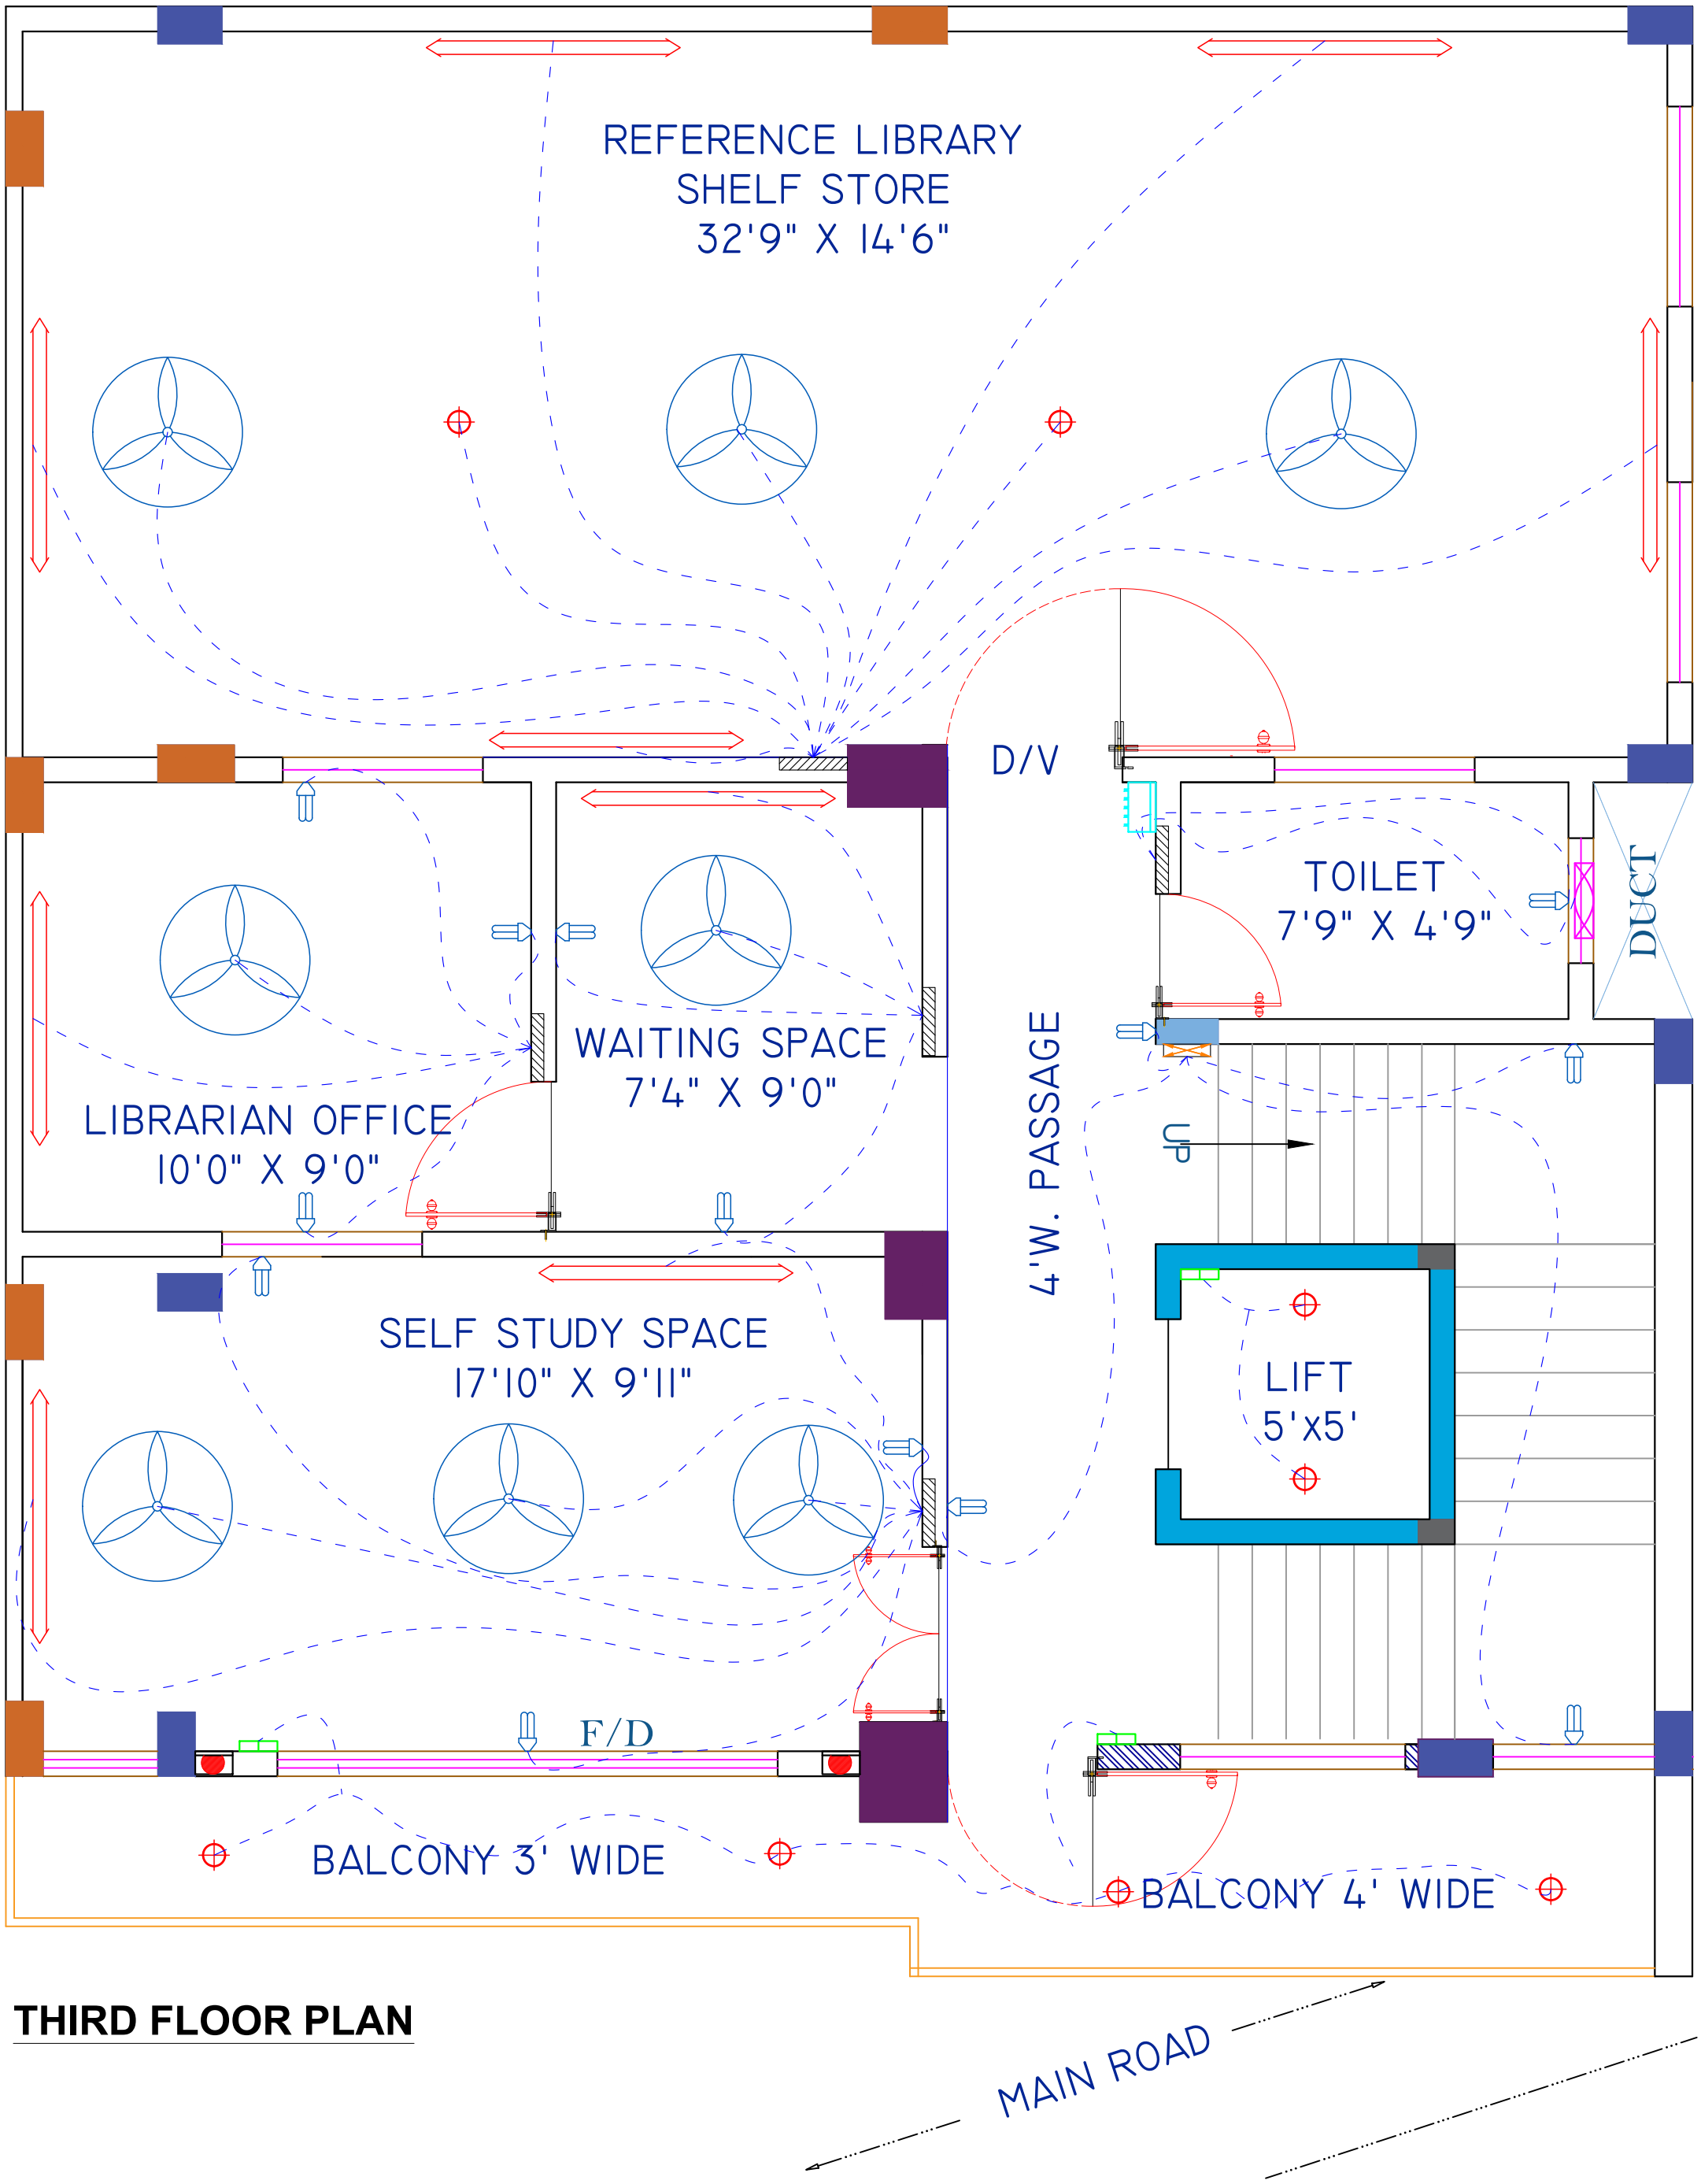

THIRD FLOOR PLAN

S
E W
N

GENERAL NOTE'S:-

PROJECT DETAILS:-

PROPOSED THIRD FLOOR ARCHITECTURAL PLAN
FOR PROPOSED LIBRARY /
MAULANA MAUDUDI MEMORIAL FOUNDATION BUILDING
CTS NO.:-
SITUATED AT SARAFA BAZAR, SHAHGUNJ
TQ. & DIST. AURANGABAD, MAHARASHTRA.

FOR:-JAMAAT-E-ISLAMI HIND, AURANGABAD.

CONSULTANT

INFINITY & ASSOCIATES
ATTRIBUTES OF AUTHENTICITY
•PLANNER •RCC DESIGNER •VALUER
1st Floor, Opp. Tirupati Enclave, Silk Mills Colony, Aurangabad - 431001.
Email: inscribeinfinity@gmail.com
Web: www.infinityally.com
M : +91 9225 796 225 | +91 9422972767

SHEET NO:- 04/05

DATE:- 09 JULY 2024 | REV. : 00

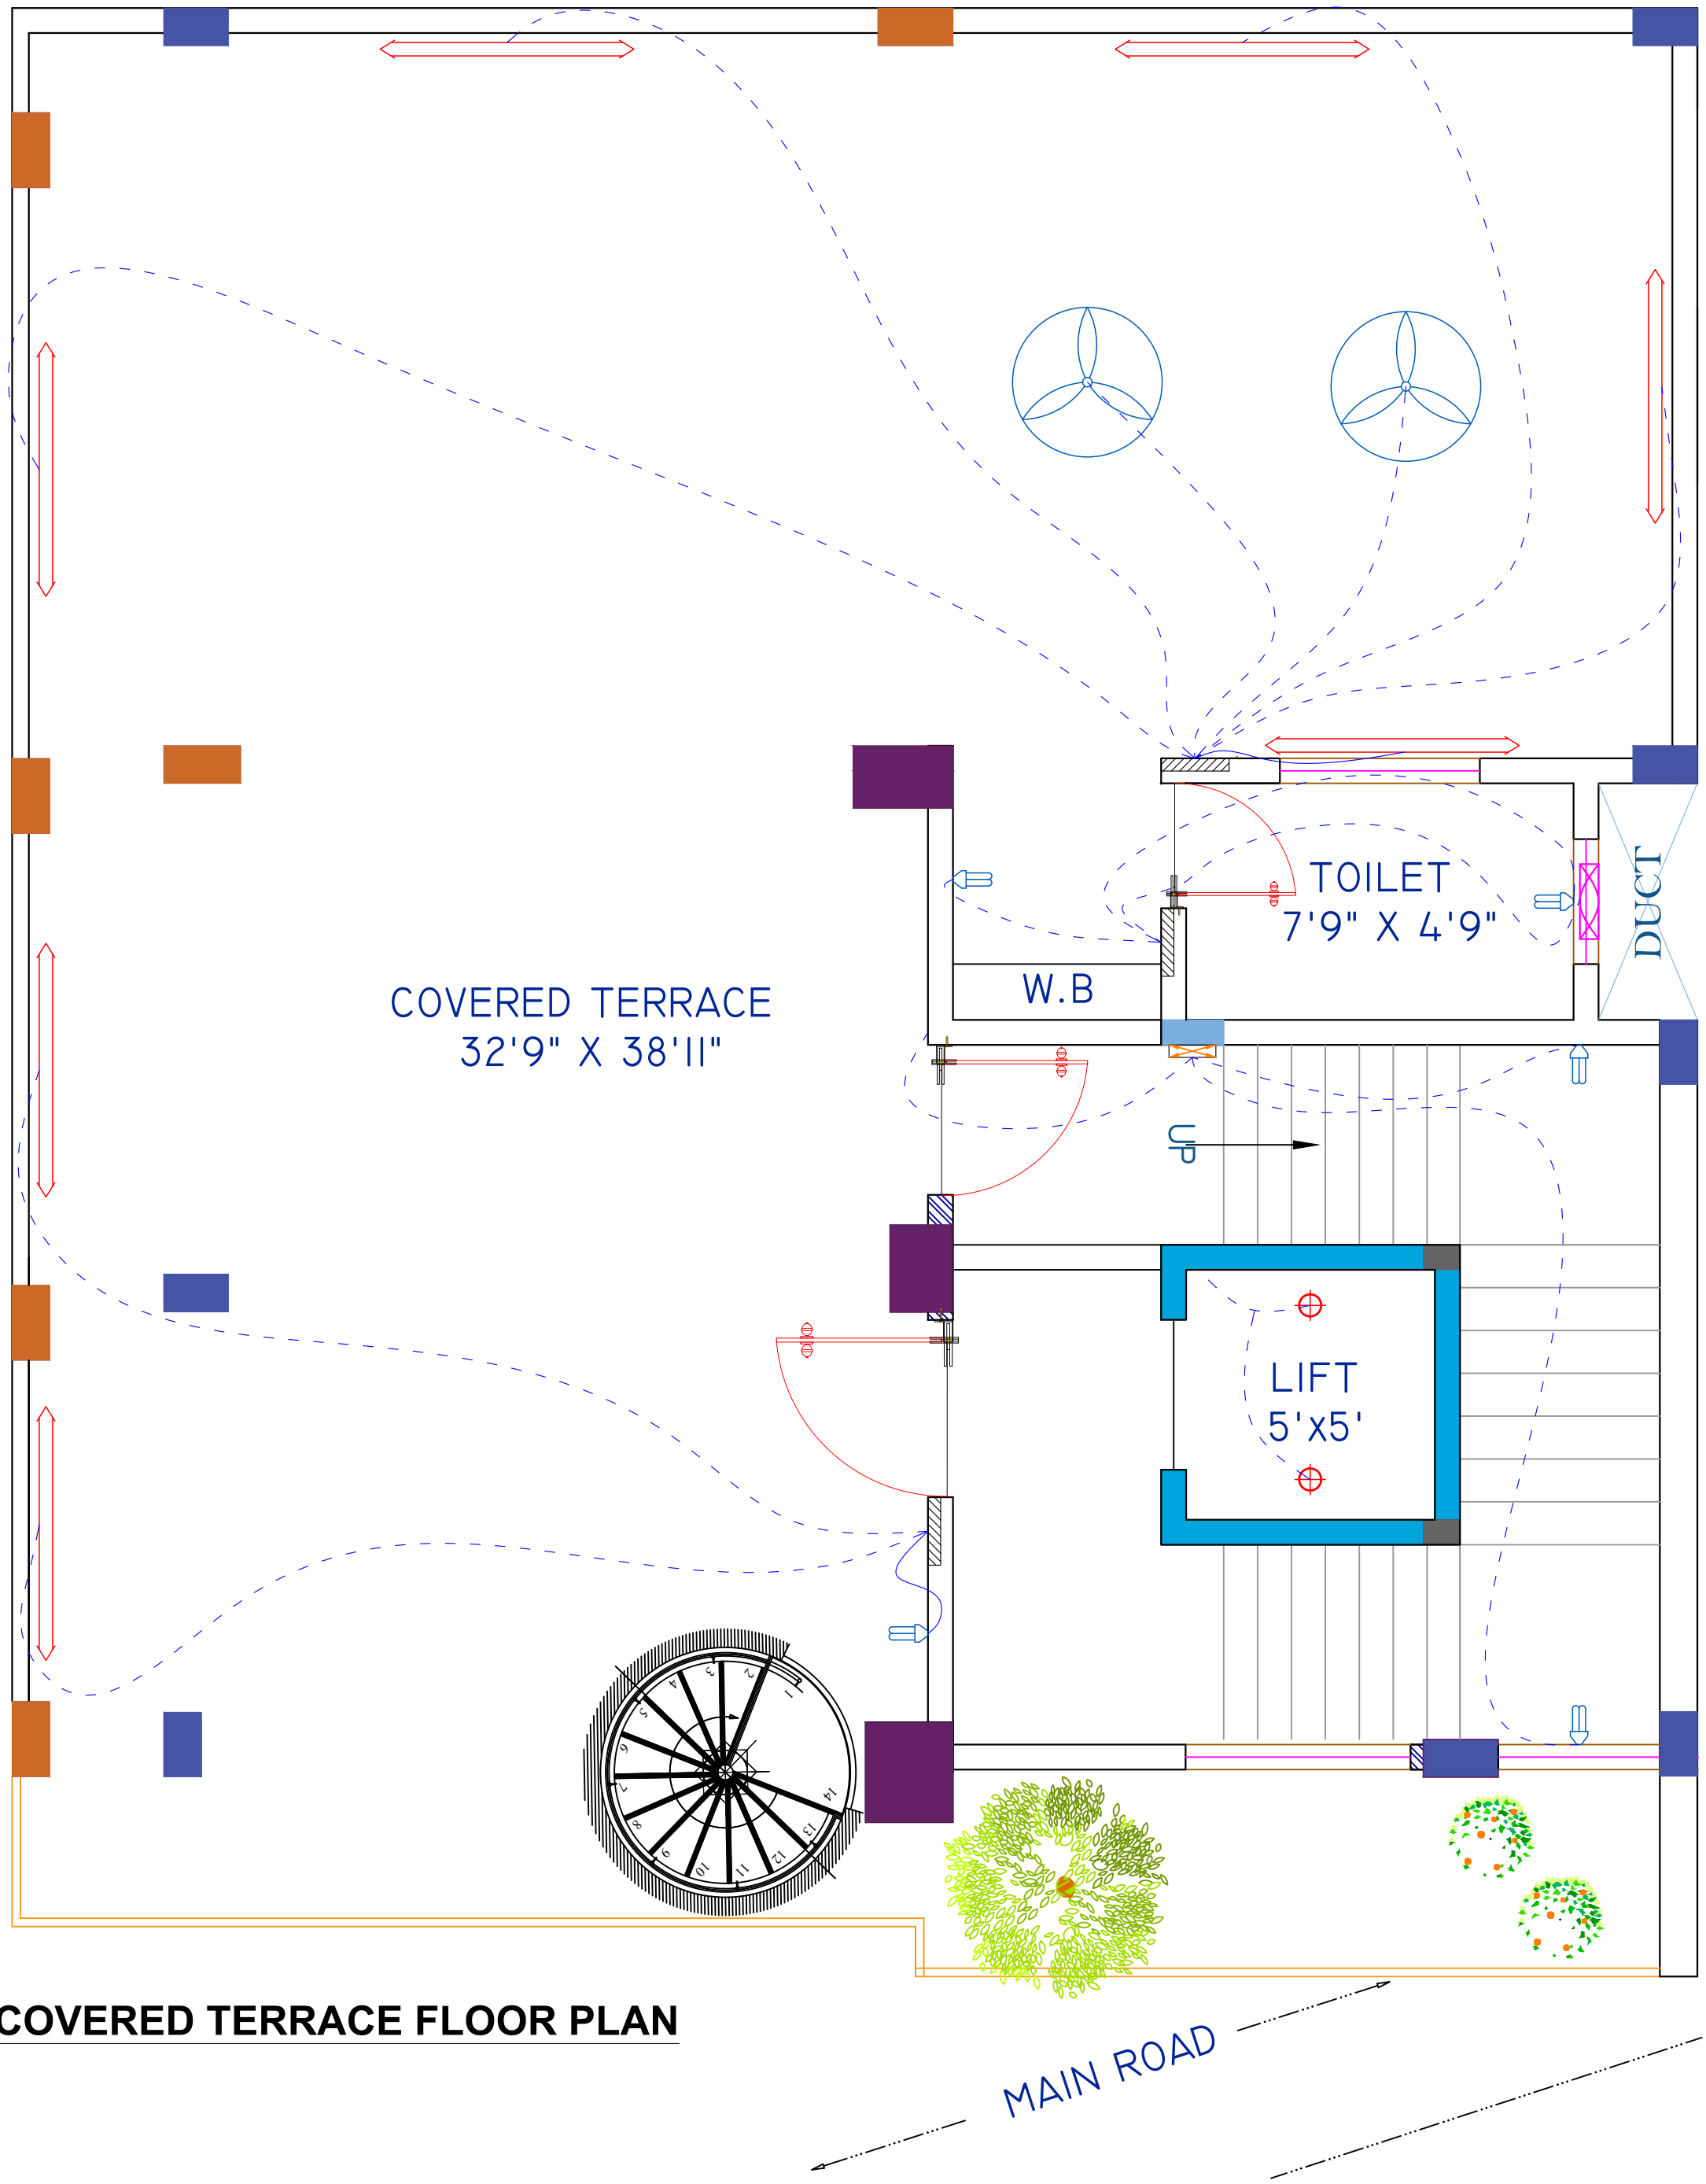

COVERED TERRACE FLOOR PLAN

S
E W
N

GENERAL NOTE'S:-

PROJECT DETAILS:-

PROPOSED COVERED TERRACE FLOOR ARCHITECTURAL PLAN
FOR PROPOSED LIBRARY /
MAULANA MAUDUDI MEMORIAL FOUNDATION BUILDING
CTS NO.:-
SITUATED AT SARAFA BAZAR, SHAHGUNJ
TQ. & DIST. AURANGABAD, MAHARASHTRA.

FOR:-JAMAAT-E-ISLAMI HIND, AURANGABAD.

SHEET NO:- 05/05

CONSULTANT

INFINITY & ASSOCIATES
ATTRIBUTES OF AUTHENTICITY
•PLANNER •RCC DESIGNER •VALUER
1st Floor, Opp. Tirupati Enclave, Silk Mills Colony, Aurangabad - 431001.
Email: inscribeinfinity@gmail.com
Web: www.infinityally.com
M : +91 9225 796 225 | +91 9422972767

DATE:- 09 JULY 2024 | REV. : 00